

CYBERCRUISER

Toyota Land Cruiser KDJ120 – allestimento camper · tavole tecniche · rev. B

- ▶ Tav. 1 – Pianta dell’allestimento
- ▶ Tav. 2 – Sezione longitudinale A-A
- ▶ Tav. 3 – Sezione trasversale B-B
- ▶ Tav. 4 – Cucina estraibile
- ▶ Tav. 5 – Vista posteriore, cucina in uso
- ▶ R1-R6 – Render 3D dell’allestimento

Quote chiave (in cm)

vano utile 165 × 130 × 90 · pavimento a 78 da terra

piano continuo a +50 · falso pavimento 12 · serbatoio 60 L


cucina estraibile 85 × 60, corsa 60, piano a 98 da terra

scrivania 70 × 45 a +76 su braccio orientabile


pozzetto piedi 70 × 30 · letto 190 × 130 ripiegabile

tetto a soffietto +95 → 185 di altezza interna

Tav. 1 – Pianta dell’allestimento

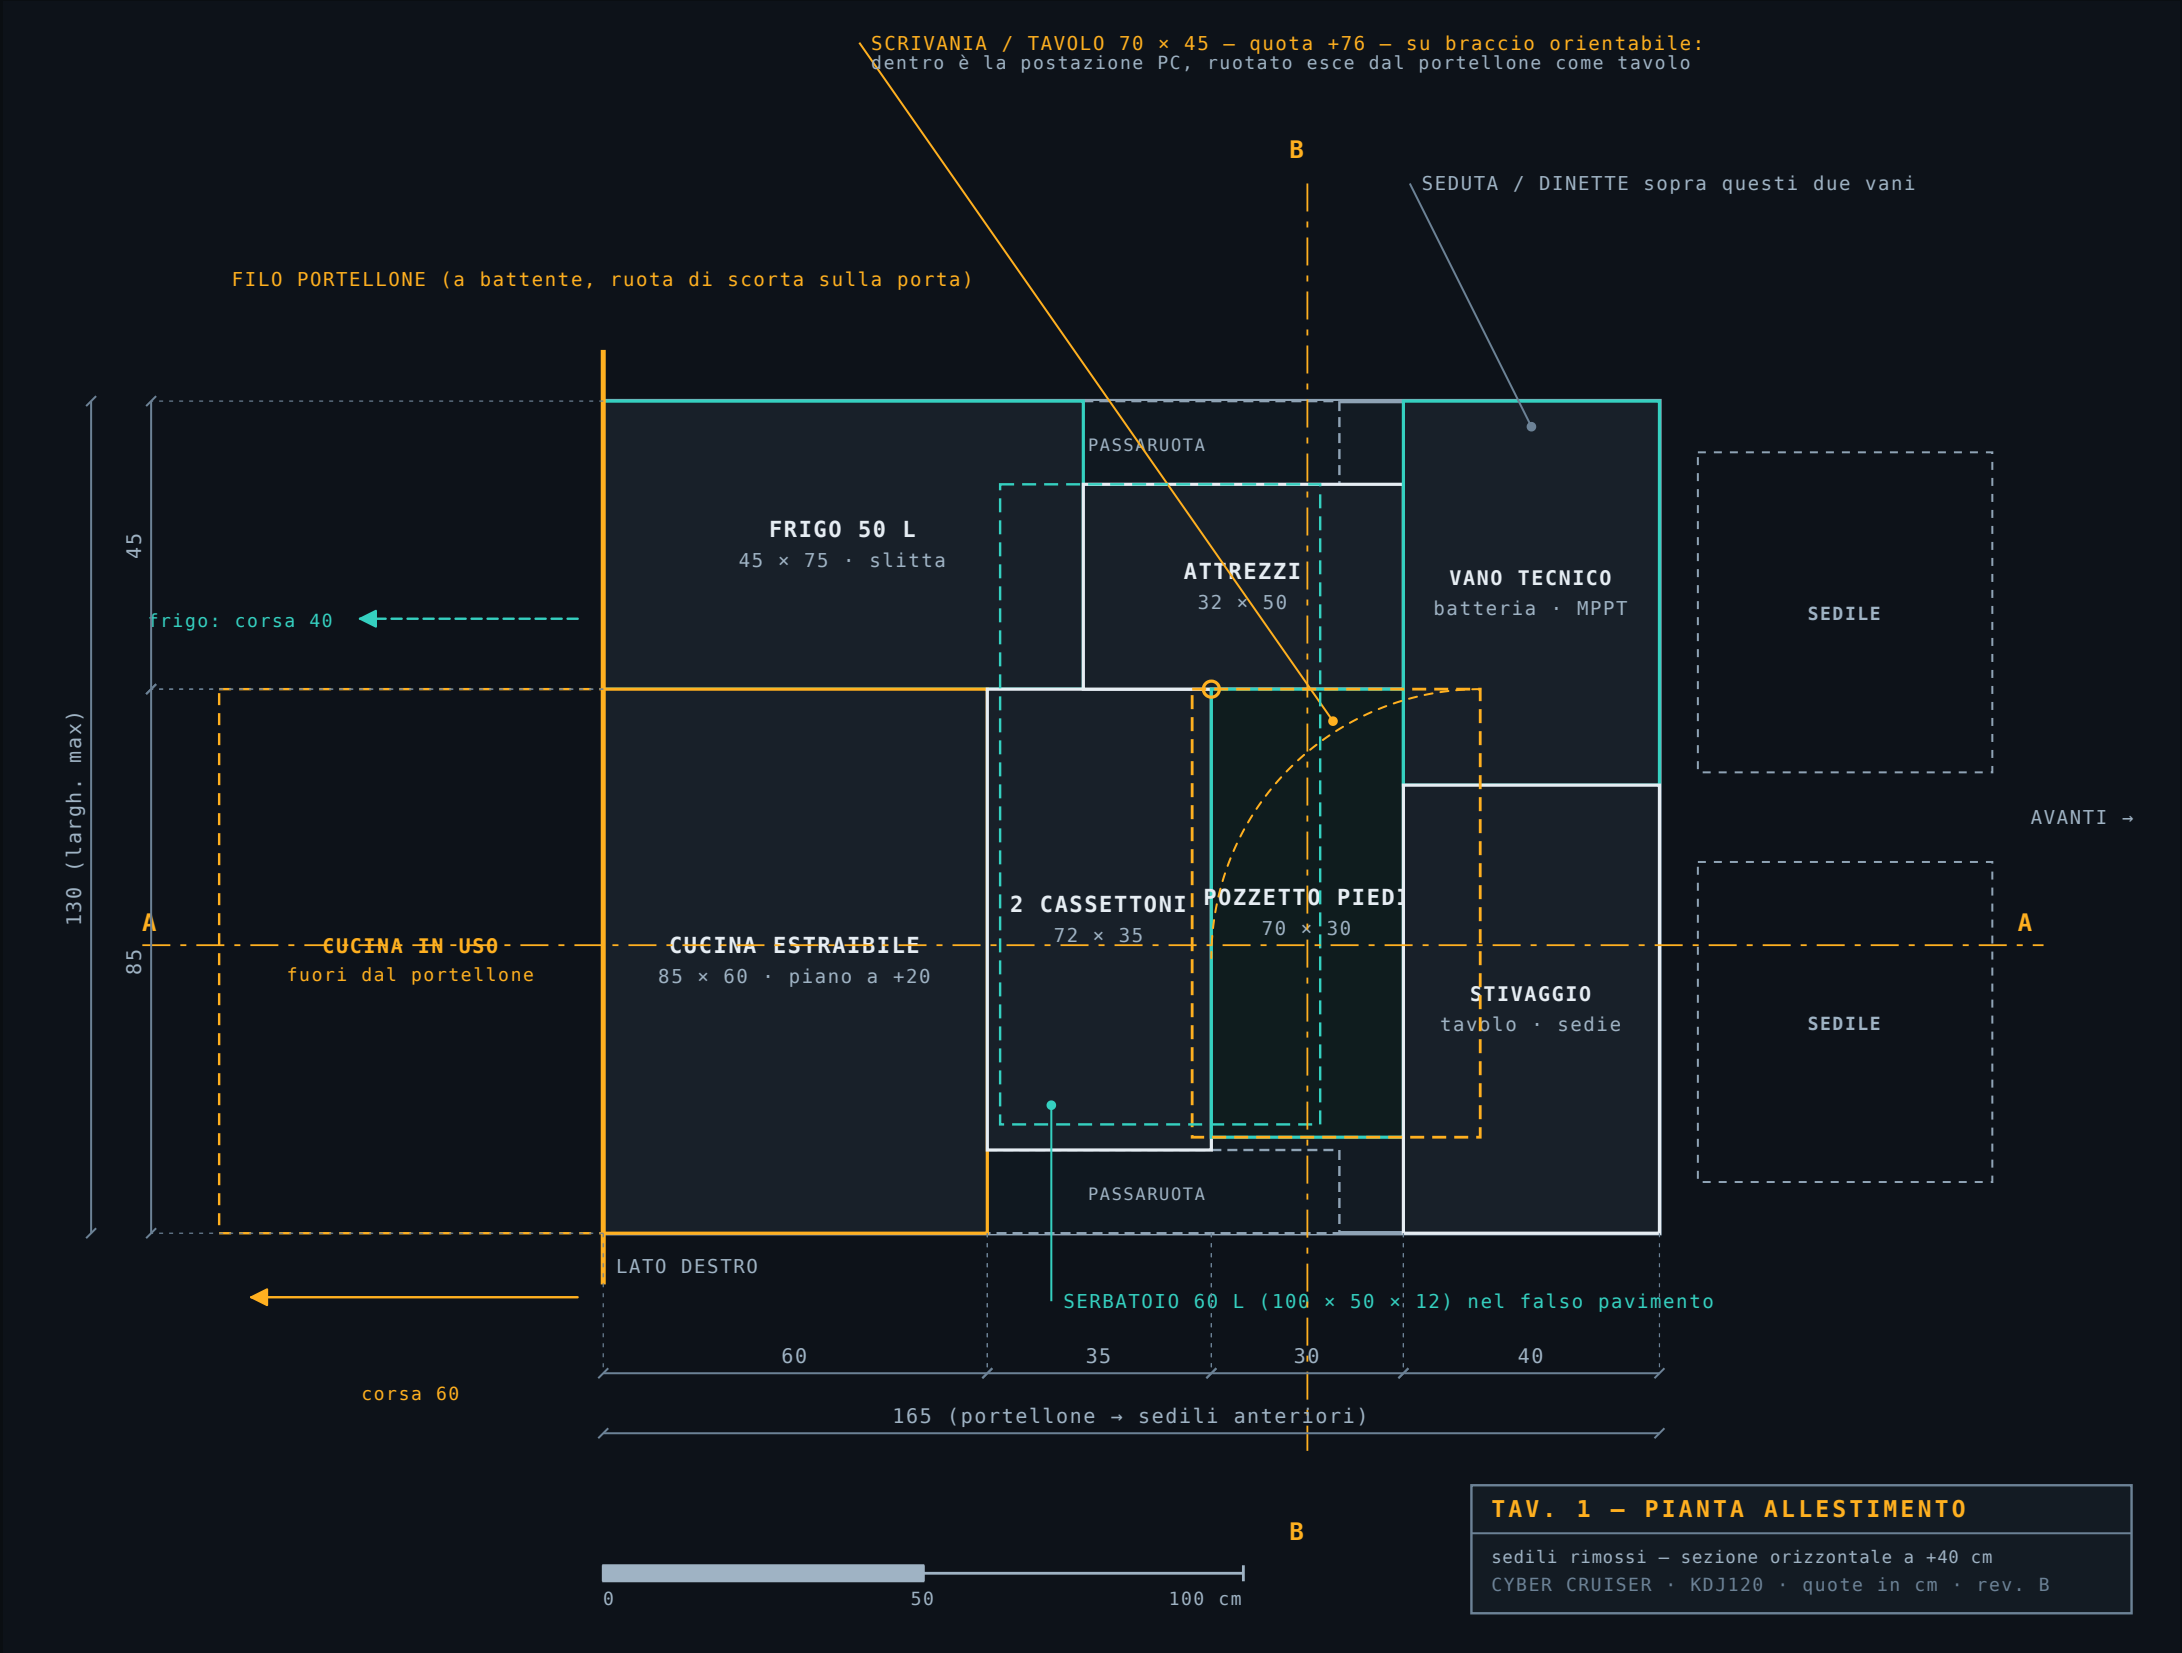


Tav. 2 – Sezione longitudinale A-A

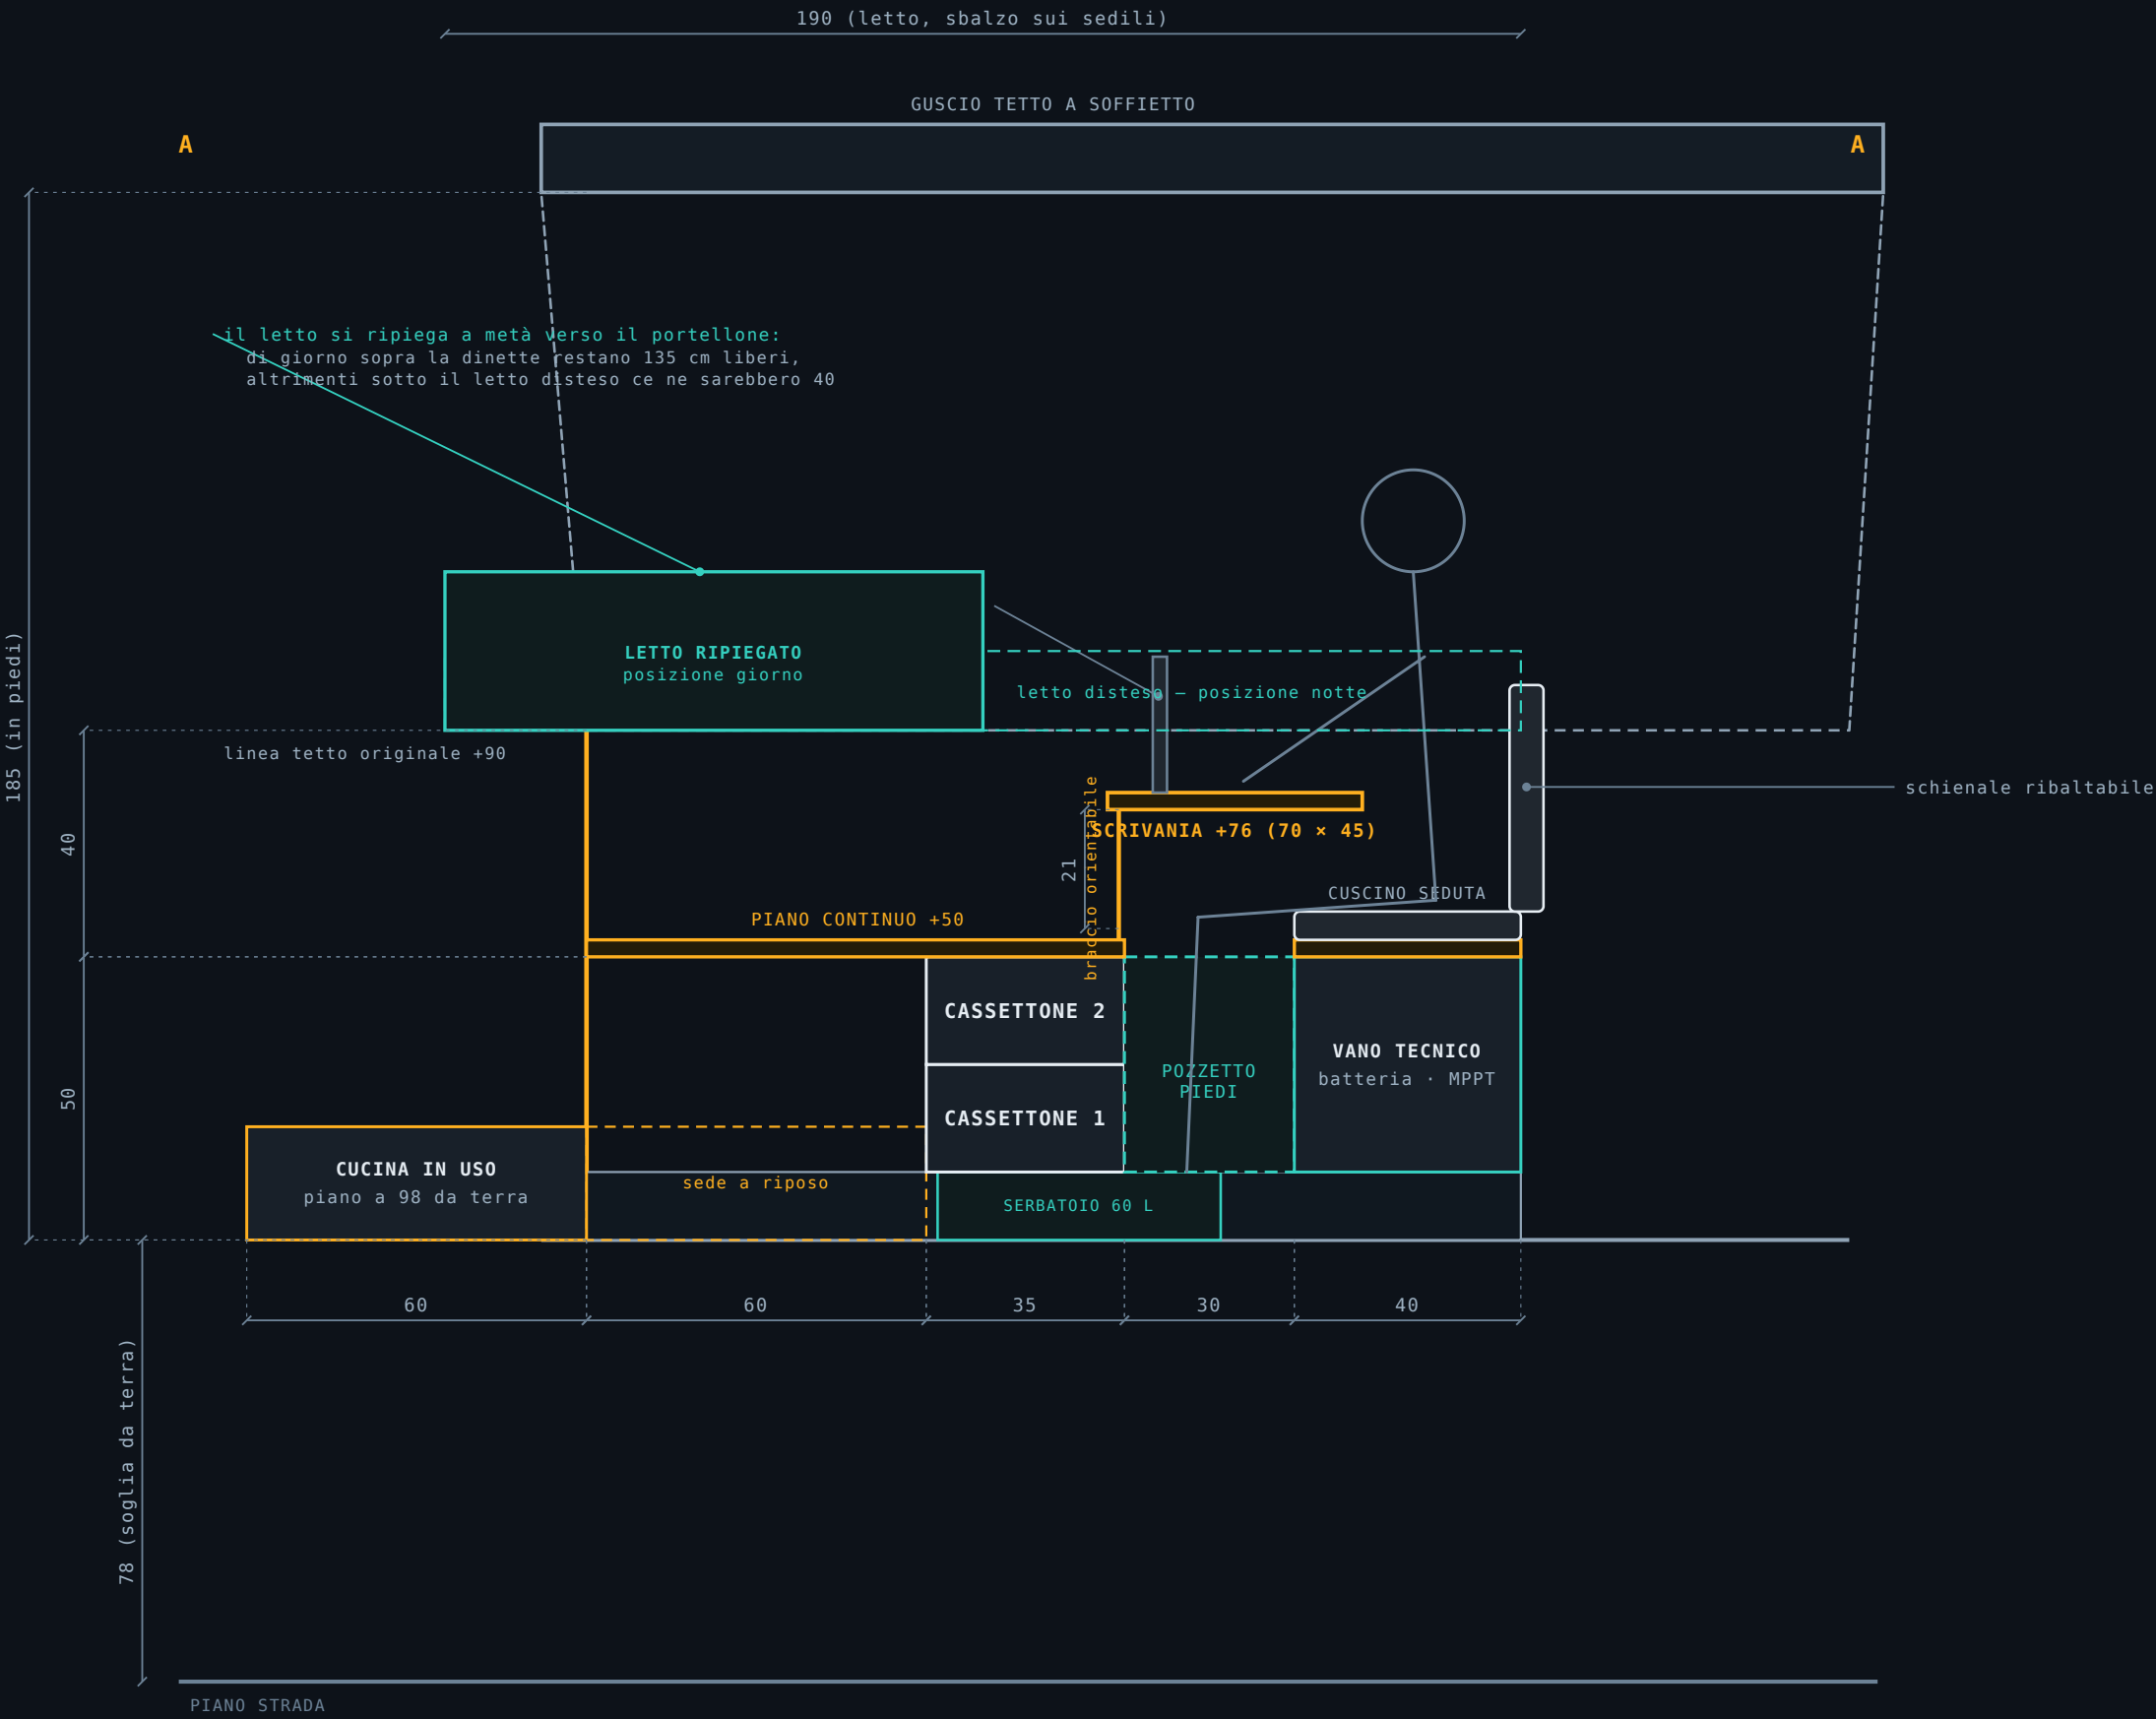

TAV. 2 – SEZIONE A-A

lato destro – cucina estratta, soffietto aperto
CYBER CRUISER · KDJ120 · quote in cm · rev. B

Tav. 3 – Sezione trasversale B-B

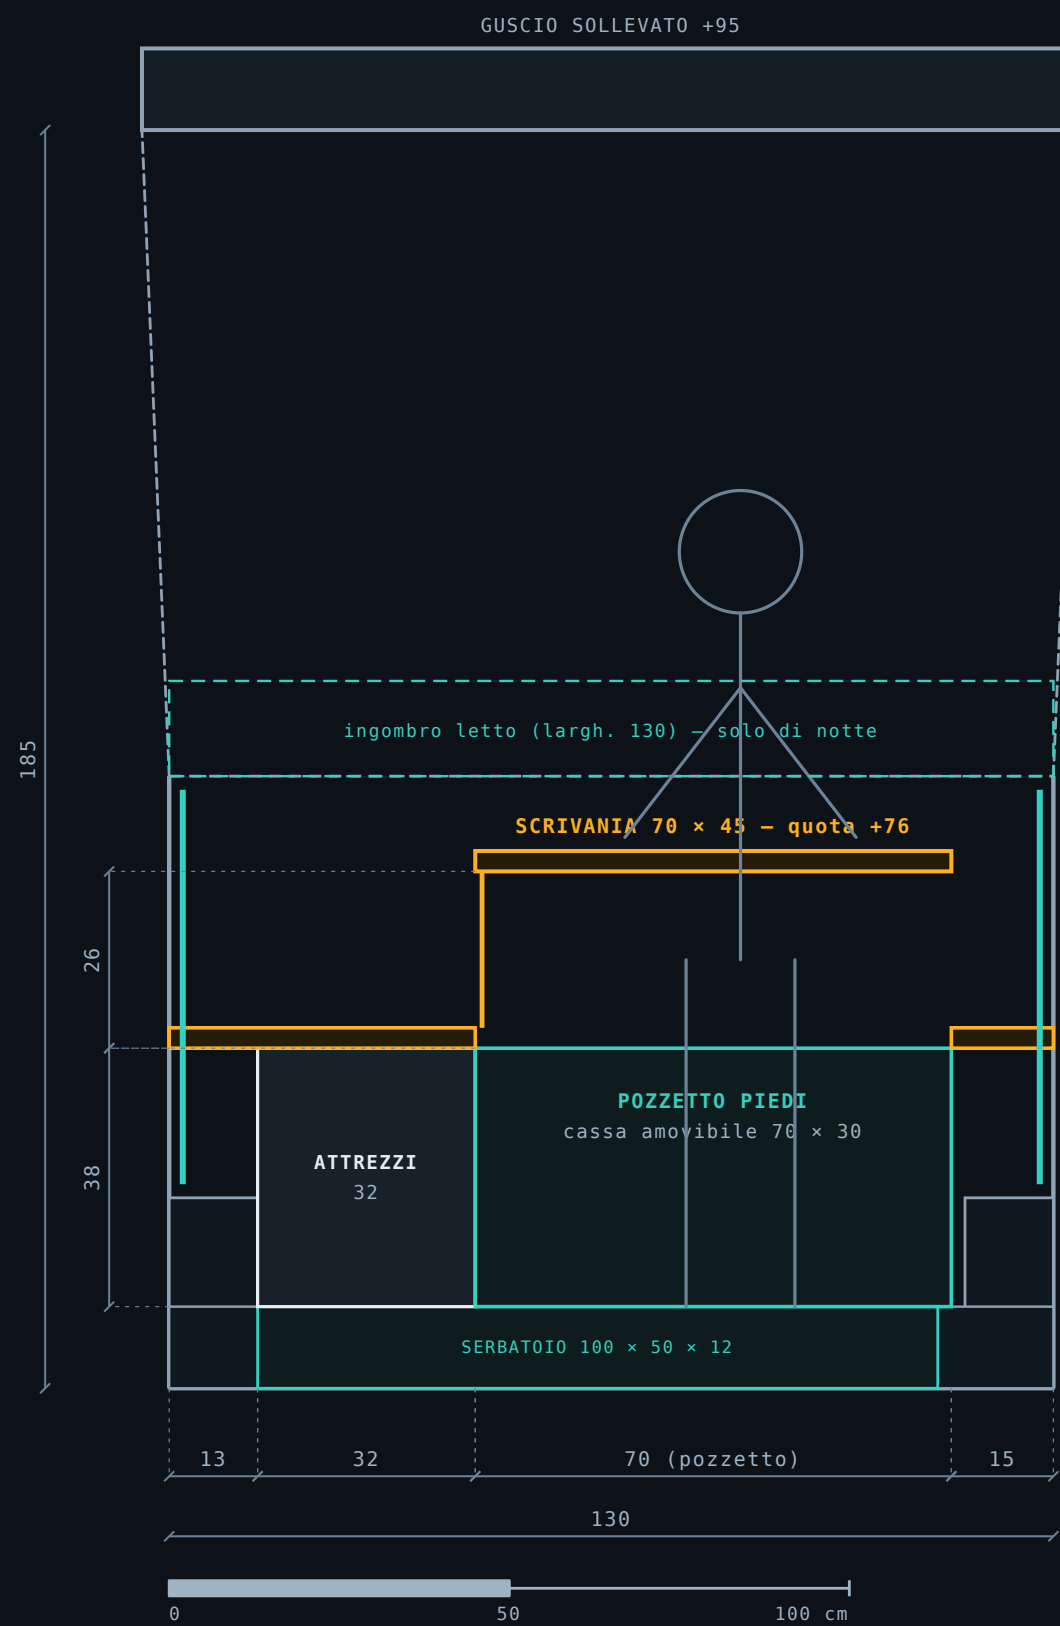

di giorno il letto è ripiegato sulla metà posteriore:
sopra la postazione restano 135 cm liberi
col soffietto chiuso ce ne sarebbero 40: si usa a tetto aperto


seduta sul piano, gambe nel pozzetto:
postura da sedia vera (38 cm seduta-piedi)

ARMAFLEX 19 mm su tutte le lamiere


TAV. 3 – SEZIONE B-B

sul pozzetto (L = 110) – postazione scrivania
CYBER CRUISER · KD1120 · quote in cm · rev. B

Tav. 4 – Cucina estraibile

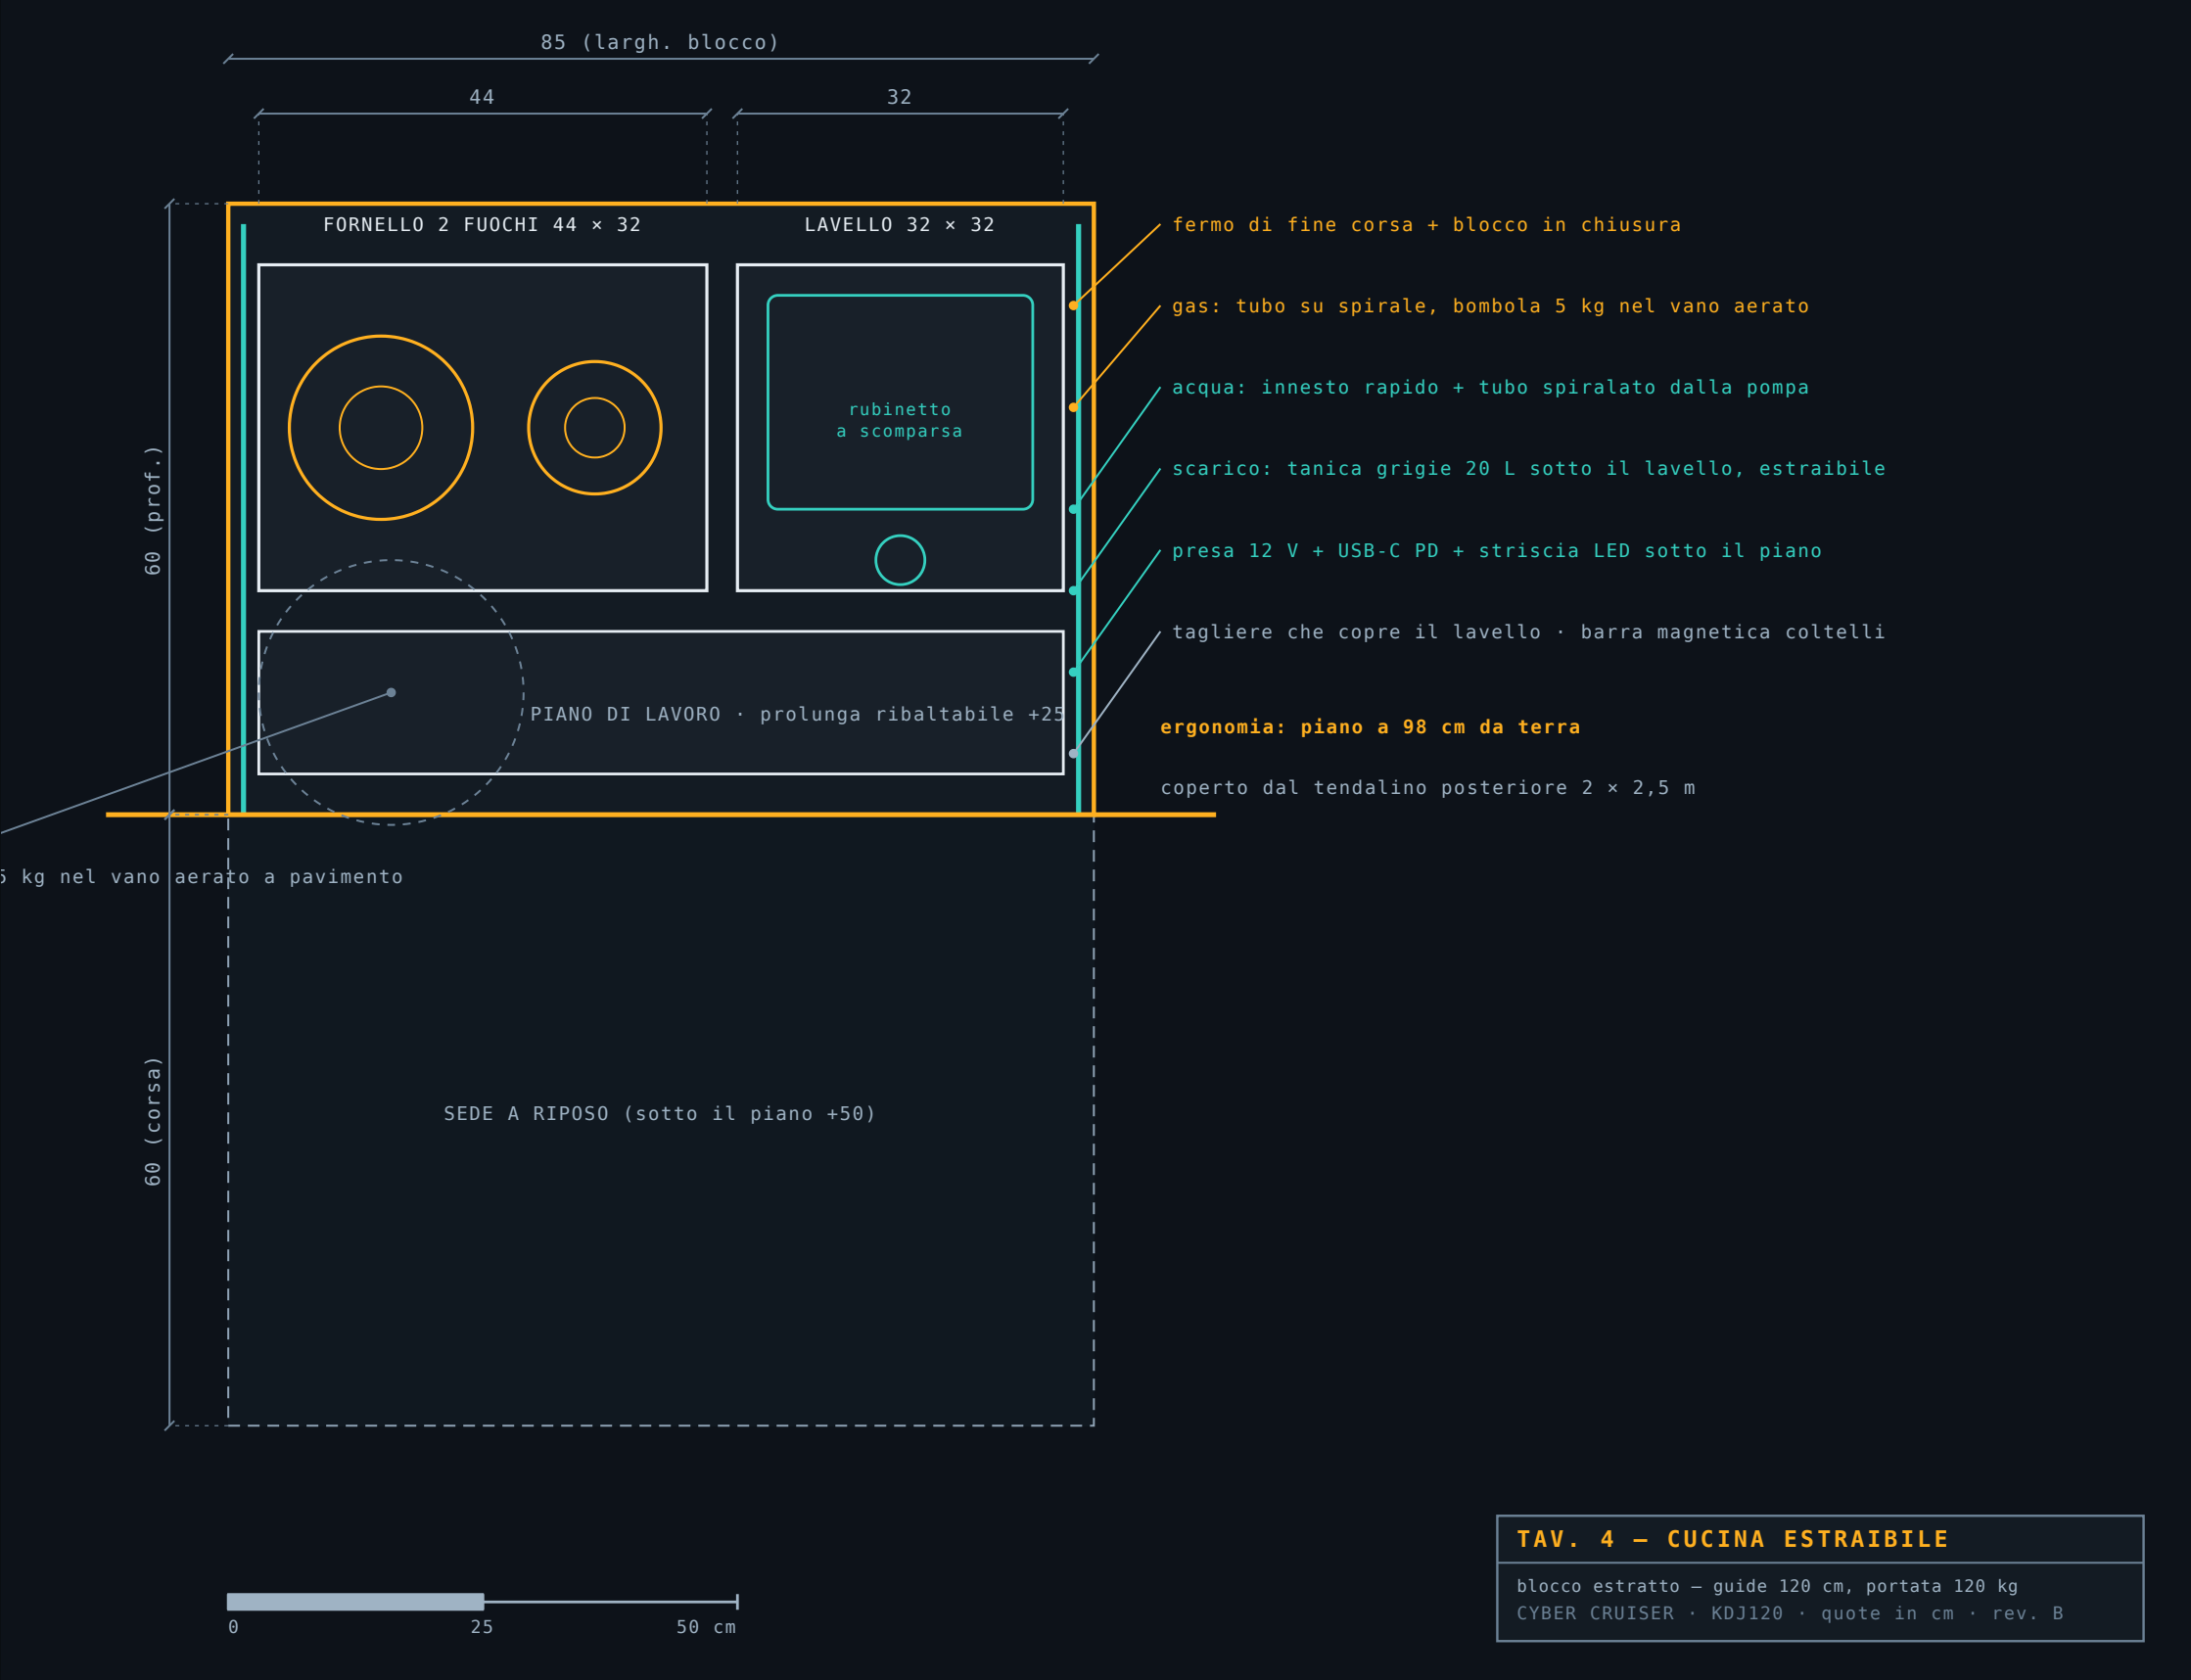

Tav. 5 – Vista posteriore, cucina in uso

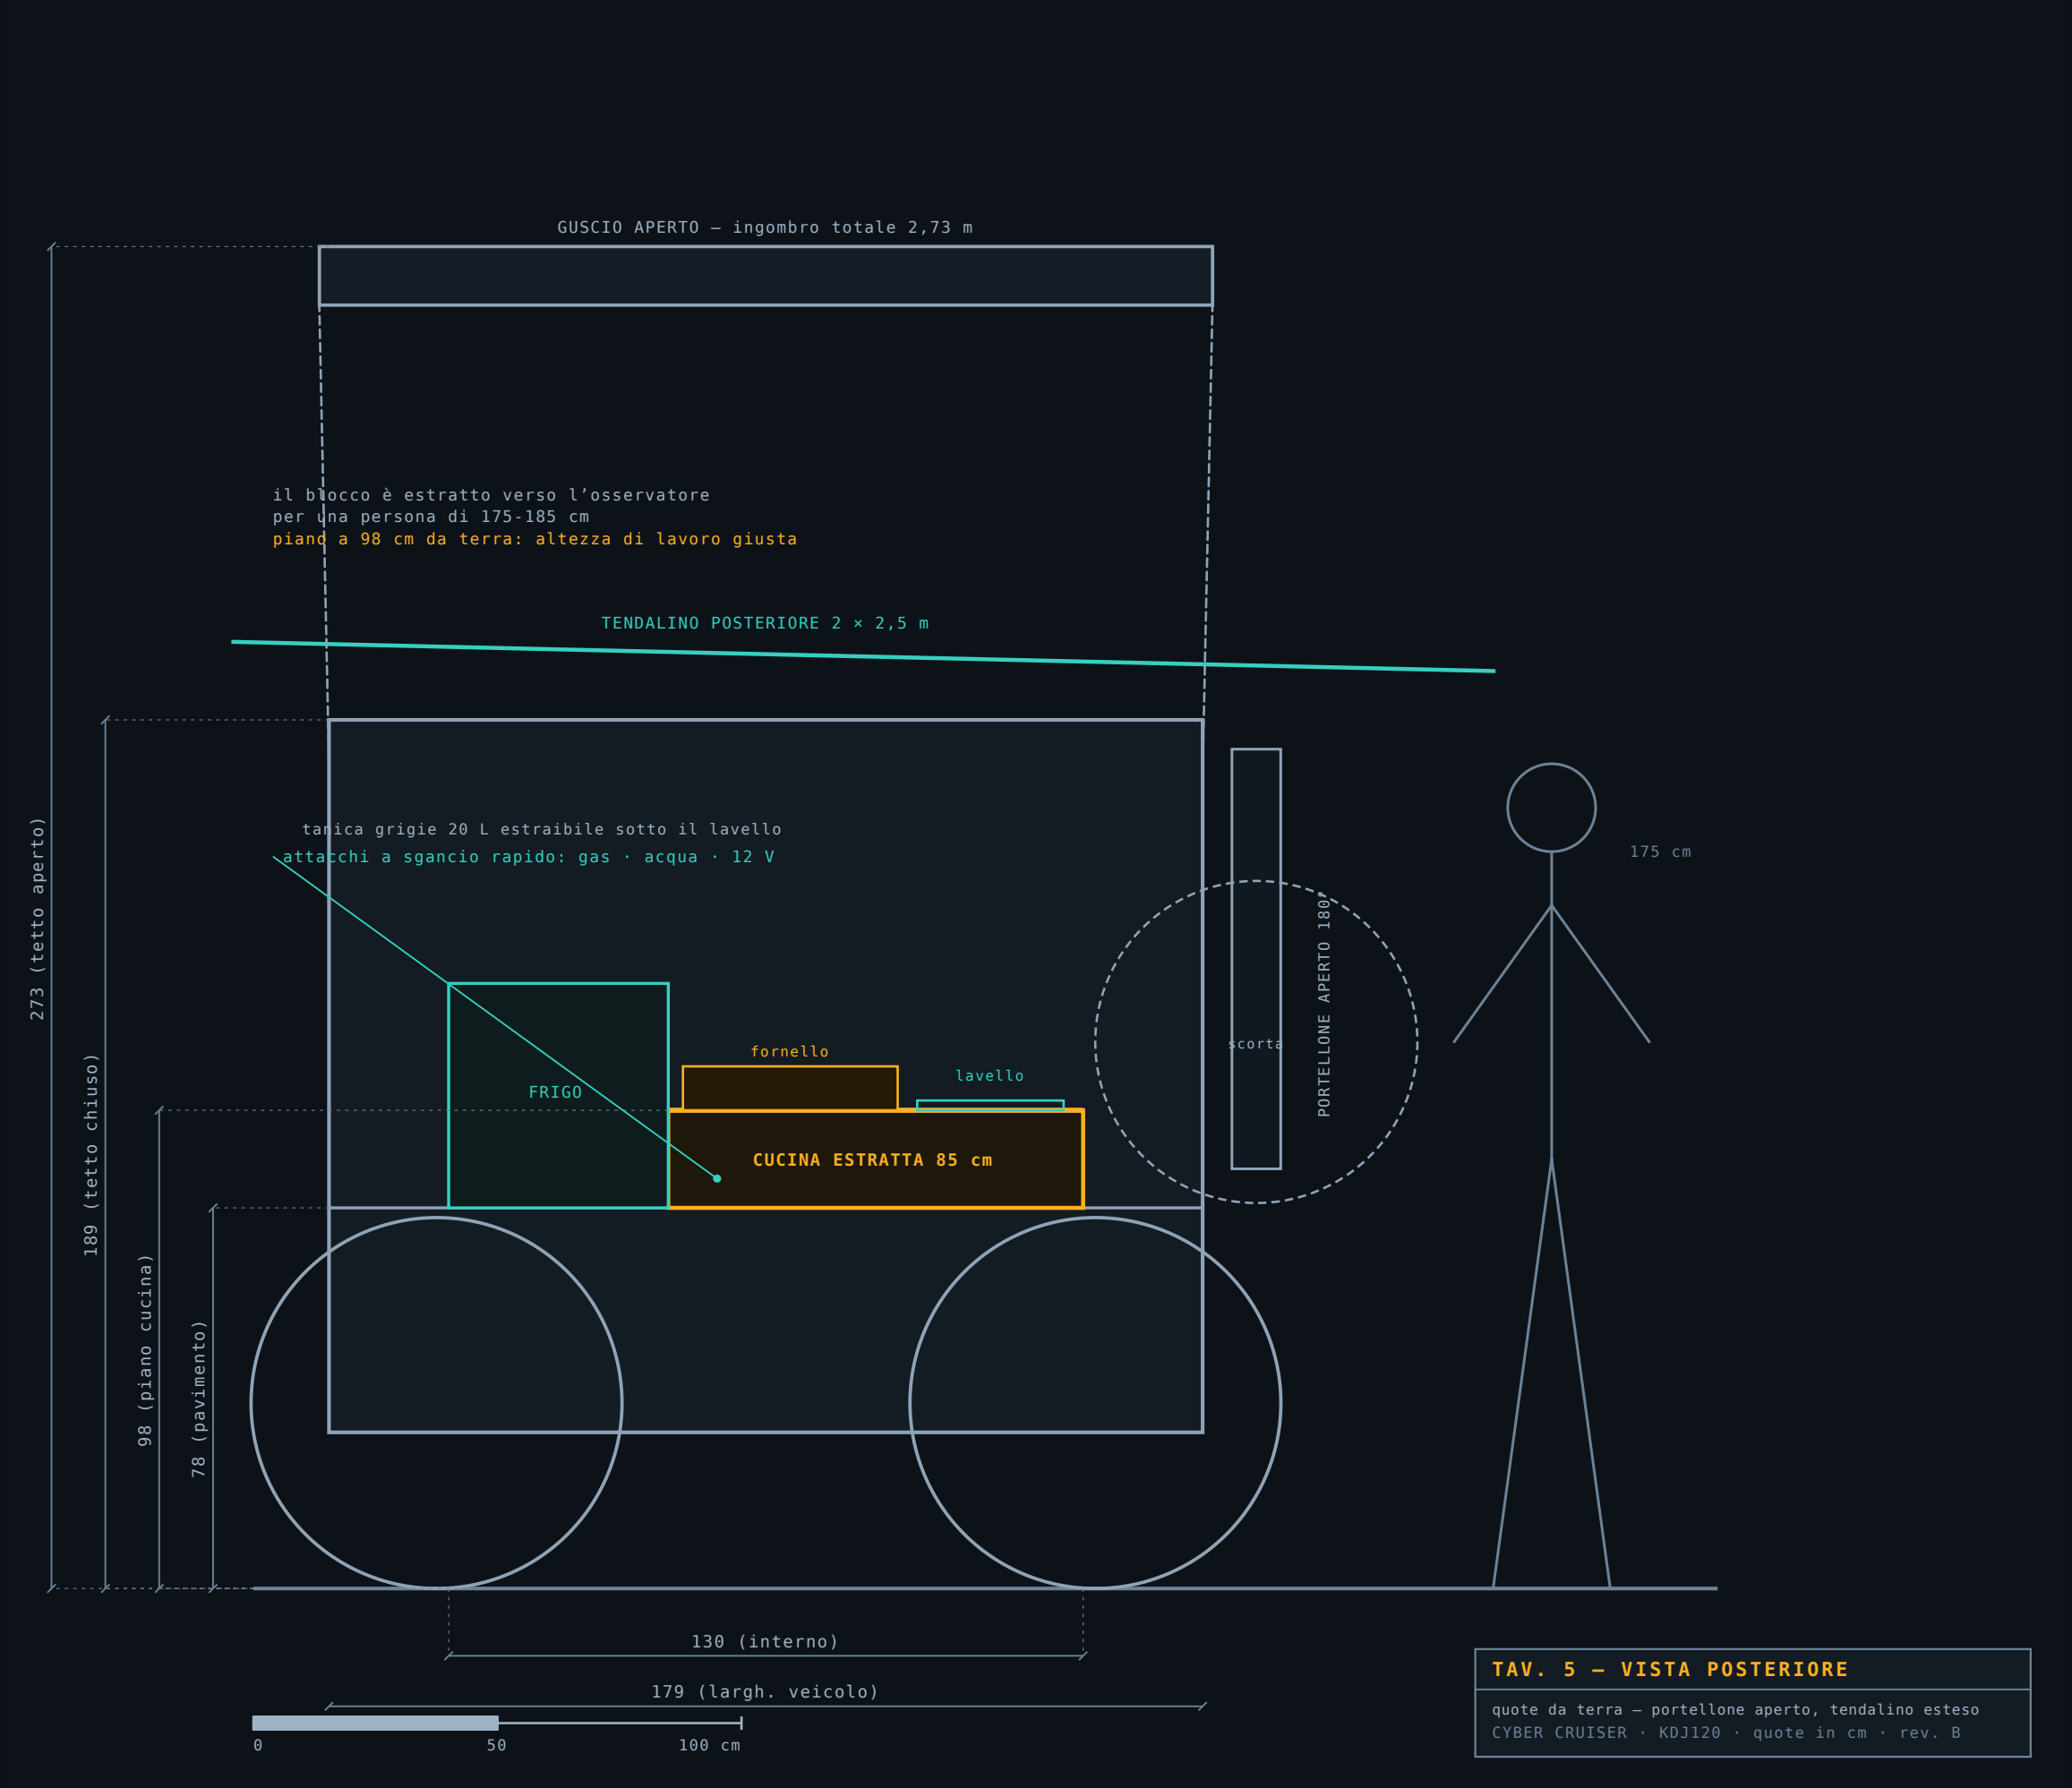

CYBERCRUISER


KDJ120 · modello 3D dell'allestimento · quote in cm

Trascina per ruotare · rotella per zoom

ambra = piani di lavoro e cucina

verde = acqua, freddo, letto, energia

vano 165 × 130 × 90 · pavimento a 78 da terra

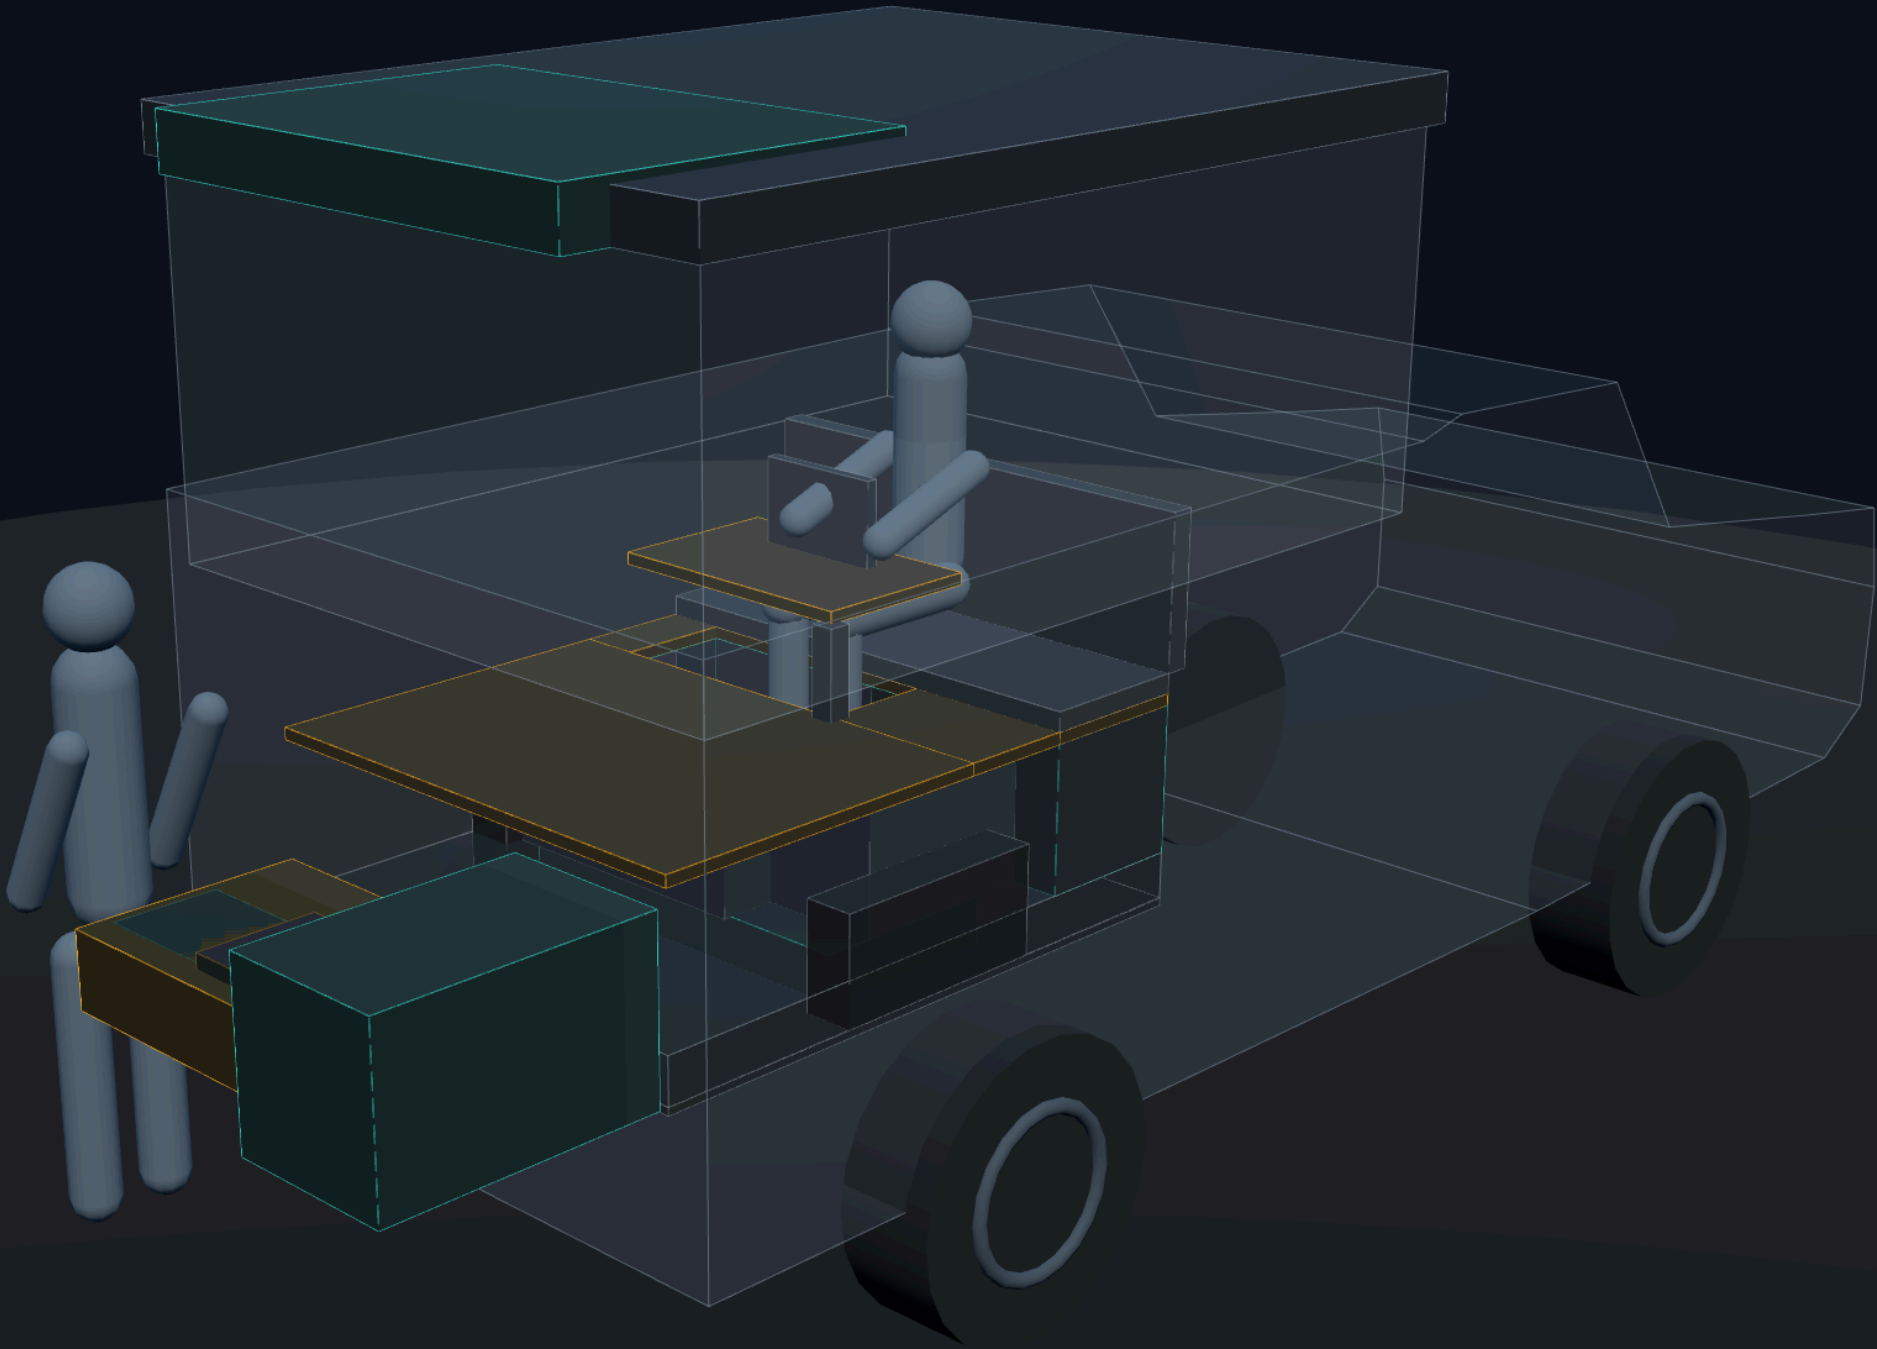

CYBERCRUISER


KDJ120 · modello 3D dell'allestimento · quote in cm


Trascina per ruotare · rotella per zoom

ambra = piani di lavoro e cucina

verde = acqua, freddo, letto, energia

vano 165 × 130 × 90 · pavimento a 78 da terra

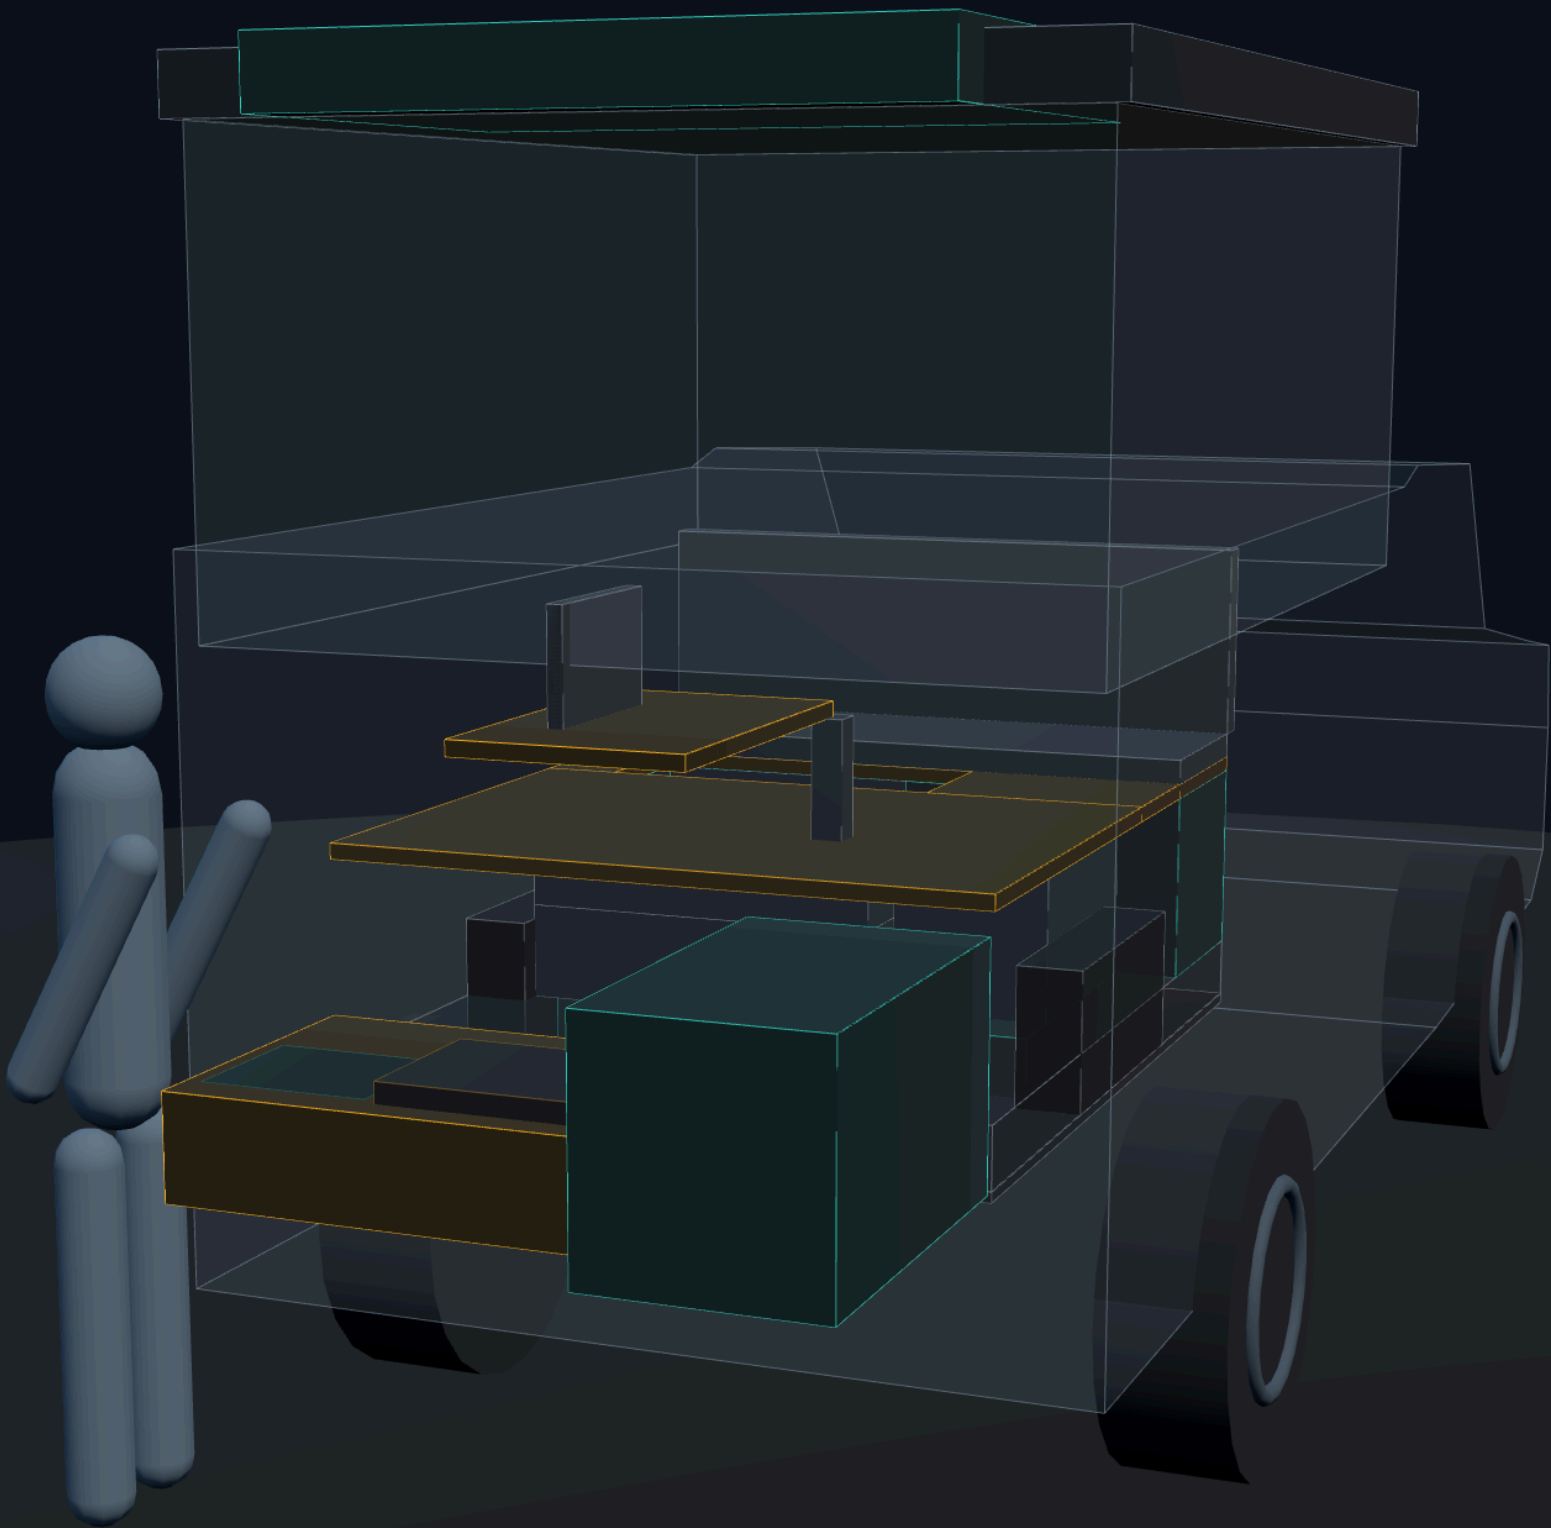

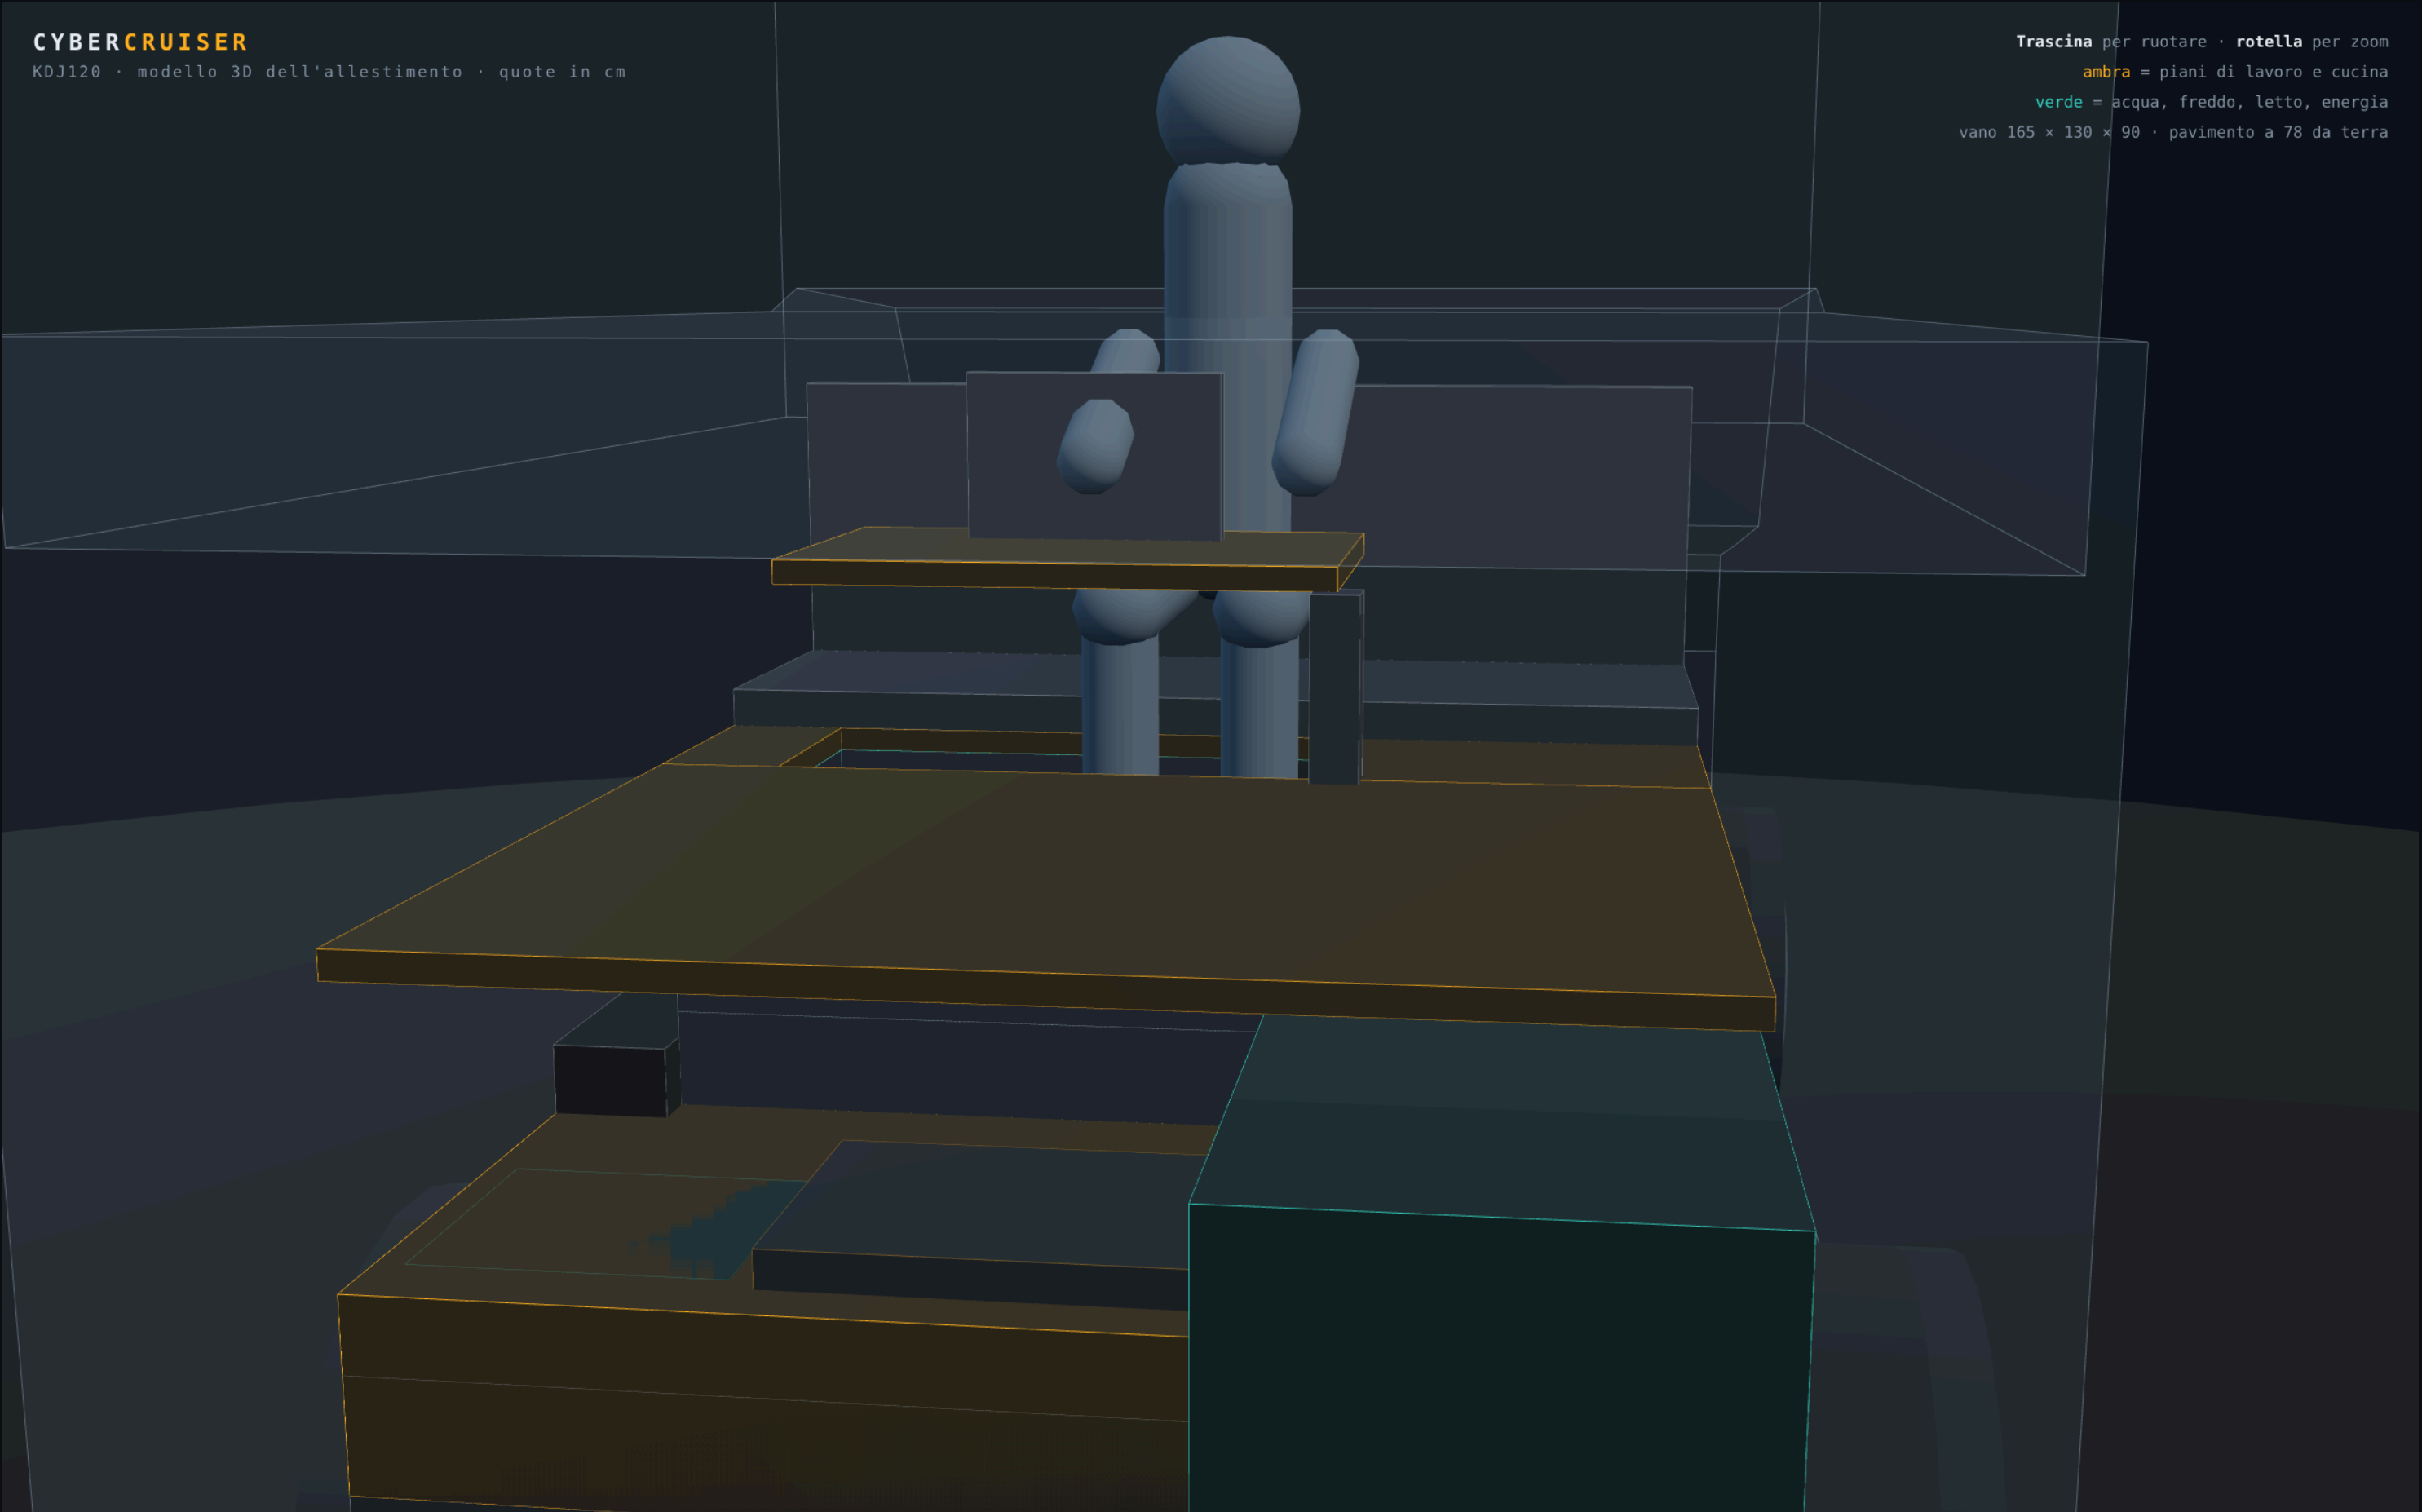

CYBERCRUISER

KDJ120 · modello 3D dell'allestimento · quote in cm

Trascina per ruotare · rotella per zoom

ambra = piani di lavoro e cucina

verde = acqua, freddo, letto, energia

vano 165 × 130 × 90 · pavimento a 78 da terra

